


PLAN TOPOGRAFIC
SCARA 1:1000
Intravilan extins conform PUZ UAT Rediu, județul Iași
Nr. cad. 70147, CFE 70147

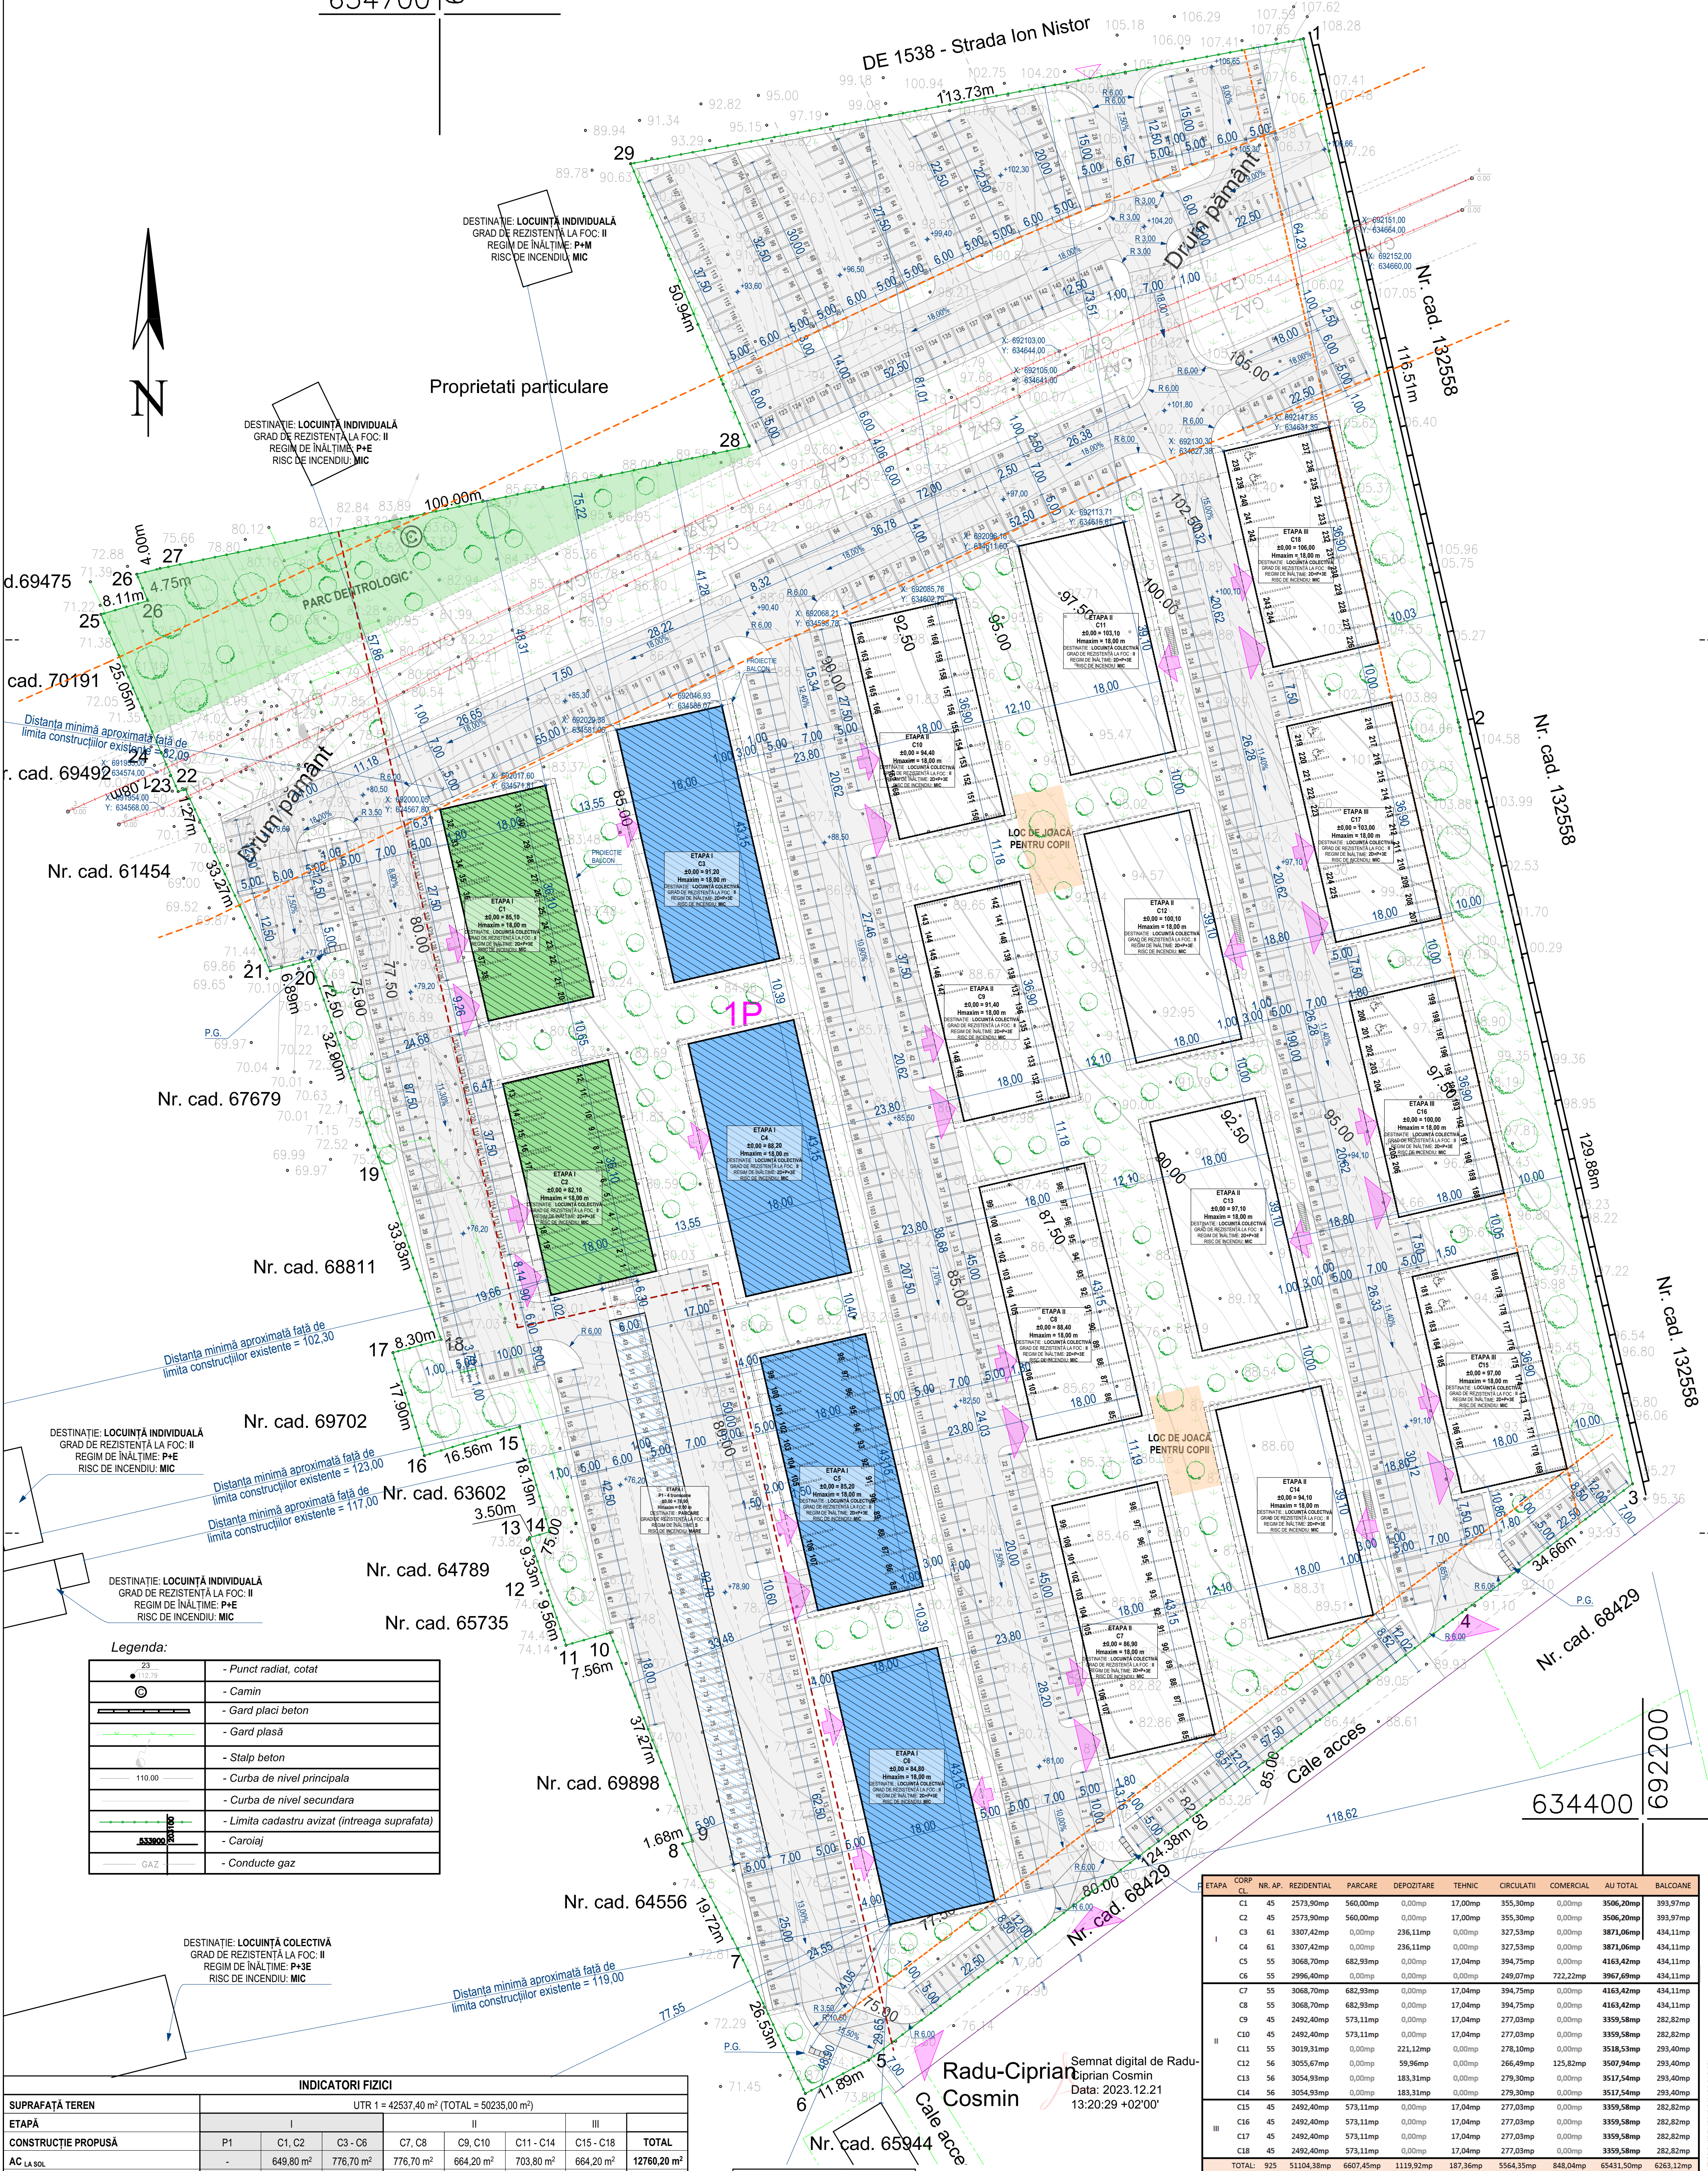

Legenda:

	- Punct radiat, cotel
	- Cămin
	- Gard placă beton
	- Gard plasă
	- Stalp beton
	- Curba de nivel principală
	- Curba de nivel secundară
	- Limita cadastru avizat (intreaga suprafață)
	- Caroiu
	- Conducte gaz


INDICATORI FIZICI								
SUPRAFAȚĂ TEREN	UTR 1 = 42537,40 m ² (TOTAL = 50235,00 m ²)							
ETAPĂ	I			II			III	
CONSTRUCȚIE PROPUȘĂ	P1	C1, C2	C3 - C6	C7, C8	C9, C10	C11 - C14	C15 - C18	TOTAL
AC LA SOL	-	649,80 m ²	776,70 m ²	776,70 m ²	664,20 m ²	703,80 m ²	664,20 m ²	12760,20 m ²
ADC, EXCLUSIV SUBSOL PENTRU CALCUL CUT	-	3898,80 m ²	4660,20 m ²	4660,20 m ²	3985,20 m ²	4222,80 m ²	3985,20 m ²	76561,20 m ²
AD	556,20 m ²	3898,80 m ²	4660,20 m ²	4660,20 m ²	3985,20 m ²	4222,80 m ²	3985,20 m ²	77116,60 m ²
VOLUM	1502,00 m ³	11306,00 m ³	13515,00 m ³	13515,00 m ³	11557,00 m ³	12246,00 m ³	11557,00 m ³	159540,00 m ³
REGIM DE ÎNĂLȚIME	S	2D+P+3E	2D+P+3E	2D+P+3E	2D+P+3E	2D+P+3E	2D+P+3E	2D+P+3E
POT	-	1,53 %	1,83 %	1,82 %	1,56 %	1,65 %	1,56 %	30,00 %
CUT	-	0,09	0,11	0,11	0,09	0,10	0,09	1,80
ÎNĂLȚIME LA ATIC	-	18,00 m	18,00 m	18,00 m	18,00 m	18,00 m	18,00 m	18,00 m
ÎNĂLȚIME MAXIMĂ	-	18,00 m	18,00 m	18,00 m	18,00 m	18,00 m	18,00 m	18,00 m
NR. LOCURI DE PARCARE - SUBTERAN	36	19	23 (C5)	23	19	-	19	258
NR. LOCURI DE PARCARE - SUPRATERAN	682							
SPAȚIU VERDE	15501,80 m ² (30,85% din Steren = 50235,00 m ²)							
ALEI, TROTUARE, TERASE	4842,00 m ²							
CAROSABIL, PARCARE	17131,00 m ²							

LEGENDA	
CLĂDIRE	C1, C2
PROPUȘĂ	C3-C6
CLĂDIRI PROPUSE - ETAPA II, III	
ALEI, TERASE, TROTUARE, P.G.	
SPAȚIU VERDE	
CAROSABIL, PARCARE	
LIMITĂ TEREN PROPRIETATE	
LIMITĂ UTR c. PUZ	
ZONĂ DE PROTECȚIE	
CONDUCTĂ GAZ	
ACCES AUTO	
ACCES PIETONAL	

Radu-Ciprian Cosmin
Semnat digital de Radu-Ciprian Cosmin
Data: 2023.12.21
13:20:29 +02'00'

ETAPA	CORP CL	NR. AP.	REZIDENTIAL	PARCARE	DEPOZITARE	TEHNIC	CIRCULAȚIE	COMERCIAL	AU TOTAL	BALCOANE
I	C1	45	2573,30mp	560,00mp	0,00mp	17,00mp	355,30mp	0,00mp	3506,20mp	393,97mp
	C2	45	2573,30mp	560,00mp	0,00mp	17,00mp	355,30mp	0,00mp	3506,20mp	393,97mp
	C3	61	3307,42mp	0,00mp	236,11mp	0,00mp	327,53mp	0,00mp	3871,06mp	434,11mp
	C4	61	3307,42mp	0,00mp	236,11mp	0,00mp	327,53mp	0,00mp	3871,06mp	434,11mp
	C5	55	3068,70mp	682,93mp	0,00mp	17,04mp	394,75mp	0,00mp	4163,42mp	434,11mp
II	C6	55	2996,40mp	0,00mp	0,00mp	0,00mp	249,07mp	722,22mp	3967,69mp	434,11mp
	C7	55	3068,70mp	682,93mp	0,00mp	17,04mp	394,75mp	0,00mp	4163,42mp	434,11mp
	C8	55	3068,70mp	682,93mp	0,00mp	17,04mp	394,75mp	0,00mp	4163,42mp	434,11mp
	C9	45	2492,40mp	573,11mp	0,00mp	17,04mp	277,03mp	0,00mp	3359,58mp	282,82mp
	C10	45	2492,40mp	573,11mp	0,00mp	17,04mp	277,03mp	0,00mp	3359,58mp	282,82mp
III	C11	55	3019,31mp	0,00mp	221,12mp	0,00mp	278,10mp	0,00mp	3518,53mp	293,40mp
	C12	56	3055,67mp	0,00mp	59,96mp	0,00mp	266,49mp	125,82mp	3507,94mp	293,40mp
	C13	56	3054,93mp	0,00mp	183,31mp	0,00mp	279,30mp	0,00mp	3517,54mp	293,40mp
	C14	56	3054,93mp	0,00mp	183,31mp	0,00mp	279,30mp	0,00mp	3517,54mp	293,40mp
	C15	45	2492,40mp	573,11mp	0,00mp	17,04mp	277,03mp	0,00mp	3359,58mp	282,82mp
TOTAL:	C16	45	2492,40mp	573,11mp	0,00mp	17,04mp	277,03mp	0,00mp	3359,58mp	282,82mp
	C17	45	2492,40mp	573,11mp	0,00mp	17,04mp	277,03mp	0,00mp	3359,58mp	282,82mp
	C18	45	2492,40mp	573,11mp	0,00mp	17,04mp	277,03mp	0,00mp	3359,58mp	282,82mp

Planul topografic se va utiliza doar în scopul solicitat respectiv "Construire 6 locuințe colective C1-C6, amenajare parcare și spații comerciale" (Certificat de urbanism nr. 194 din 23.06.2023 eliberat de Primăria comunei Rediu) și va fi însoțit de Procesul Verbal de Recepție nr. 8041 / 2023

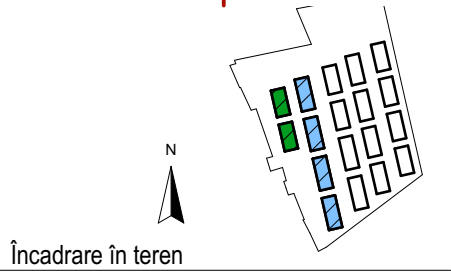

CLASA DE IMPORTANȚĂ: "III"
CATEGORIA DE IMPORTANȚĂ: "C"
GRAD DE REZISTENȚĂ LA FOC: "III"

verificator				REFERAT DE VERIFICARE NR.			
VERIFICATOR/ EXPERT	NUME	SEMNTURA	CERINTA	REFERAT/EXPERTIZA NR./DATA			
	S.C. CAD S.R.L.			S.C. TALA SAPHIRE S.R.L.			
	J22/88/2008; CUI: 23038080			Jud. Iași, com. Rediu, satul Rediu, nr. cad. 70147			
SPECIFICAȚIE	NUME	SEMNTATURA	SCARA:	CONSTRUIRE 6 LOCUINȚE COLECTIVE C1-C6, AMENAJARE PARCARE ȘI SPAȚII COMERCIALE			
ȘEF PROIECT	arh. Ovidiu M. MURGU		1:500	FAZA: DTAC			
PROIECTAT	arh. Ovidiu M. MURGU		DATA:	PLAN DE SITUAȚIE, SISTEMATIZARE VERTICALĂ, ÎMPREJURIMILE			
DESENAT	arh. stag. Violeta DALAS		06/2023	Plansa nr. A01			